验收工程量汇总表（旱改水）

序号	名　　称	单 位	验收工程量	备注
二	**建设内容**			
(一)	**土地平整工程**			
1	**施工面积**	亩	**685.729**	已扣减第一次占补已申报施工面积
2	**其中平整面积**	亩	**453.321**	
3	清障	m²	302218.670	
4	表土剥离土方量	m3	90664.101	
5	耕作层回填土方量	m3	77064.486	
6	外运犁底层及压实	m3	120885.468	
7	挖方量	m3	366075.200	
8	填方量	m3	30796.900	
9	挖填差	m3	335278.300	
10	1.5m田埂	m	3477.520	
11	2m田埂	m	485.000	
12	2.5m田埂	m	412.000	
13	土壤培肥	t	1631.954	每年2季、一季0.6t、连续3年
(二)	**灌溉与排水工程**			
1	生态渠I型	m	472.000	六棱块、（杉木桩5282根）
2	生态渠II型	m	188.000	卡扣砖
3	生态渠III型	m	2580.000	卡扣砖
4	3m现浇渠	m	185.000	现浇渠
5	排水沟	m	330.000	土0.5
6	截流沟	m	1052.000	
7	清淤坑塘	口	6.000	
8	坑塘清淤土方量	m3	70072.680	
9	晒干推平	m3	29780.889	
10	土方外运	m3	29780.889	
11	200pvc管	m	560.000	56处、一处10m
12	300pvc管	m	20.000	2处、一处110m
13	砖砌雨水沟	m	1504.000	砖砌、0.5m
14	DN300涵管（4m）	m	236.000	
15	DN400涵管（4m）	m	60.000	
16	DN600涵管（4m）	m	212.000	
17	DN800涵管（4m）	m	44.000	
18	环形沟I型	m	1567.000	土沟3.5m
19	环形沟II型	m	423.000	土沟4m
20	新建挡土墙I型	m	93.000	现浇
21	新建挡土墙II型	m	45.000	浆砌石
22	新建挡土墙III型		55.000	浆砌石
23	检查井	座	11.000	1m*1m*1.5m
24	进水池	座	1.000	
25	新建300波纹管	m	120.000	
26	新建泵房	座	1.000	
27	修复泵房	座	1.000	
28	泵房设备	套	2.000	
29	分水闸I型	座	1.000	砖墙（0.8m）
30	分水闸II型	座	15.000	砖墙（0.5m）
31	踏步	座	39.000	
32	新建电力线	m	145.000	
33	拆除电杆	根	58.000	拆除线路500m
34	新建电杆	根	5.000	
35	护栏网	m	11154.000	
36	砖砌花坛	m	308.400	高0.5m、宽0.24m
37	花坛灌木	株	13800.000	
38	灌木	m²	14573.290	
39	水草	斤	50000.000	
40	草籽	m²	60000.000	
41	果树（橙子树、橘子树等）	棵	2686.000	
42	农田监测设备	套	43.000	
43	电杆加固I型	根	2.000	
44	电杆加固II型	根	64.000	
45	撤水泵	个	1.000	
(三)	**田间道路工程**			
1	修复沥青路	m	1686.000	宽6m
2	新建3.5m碎石路	m	3098.000	底宽4.5m、（其中160m抛块石864m3、杉木桩400根）
3	新建3m田间道	m	4609.000	面宽3m
4	下田埠	座	23.000	

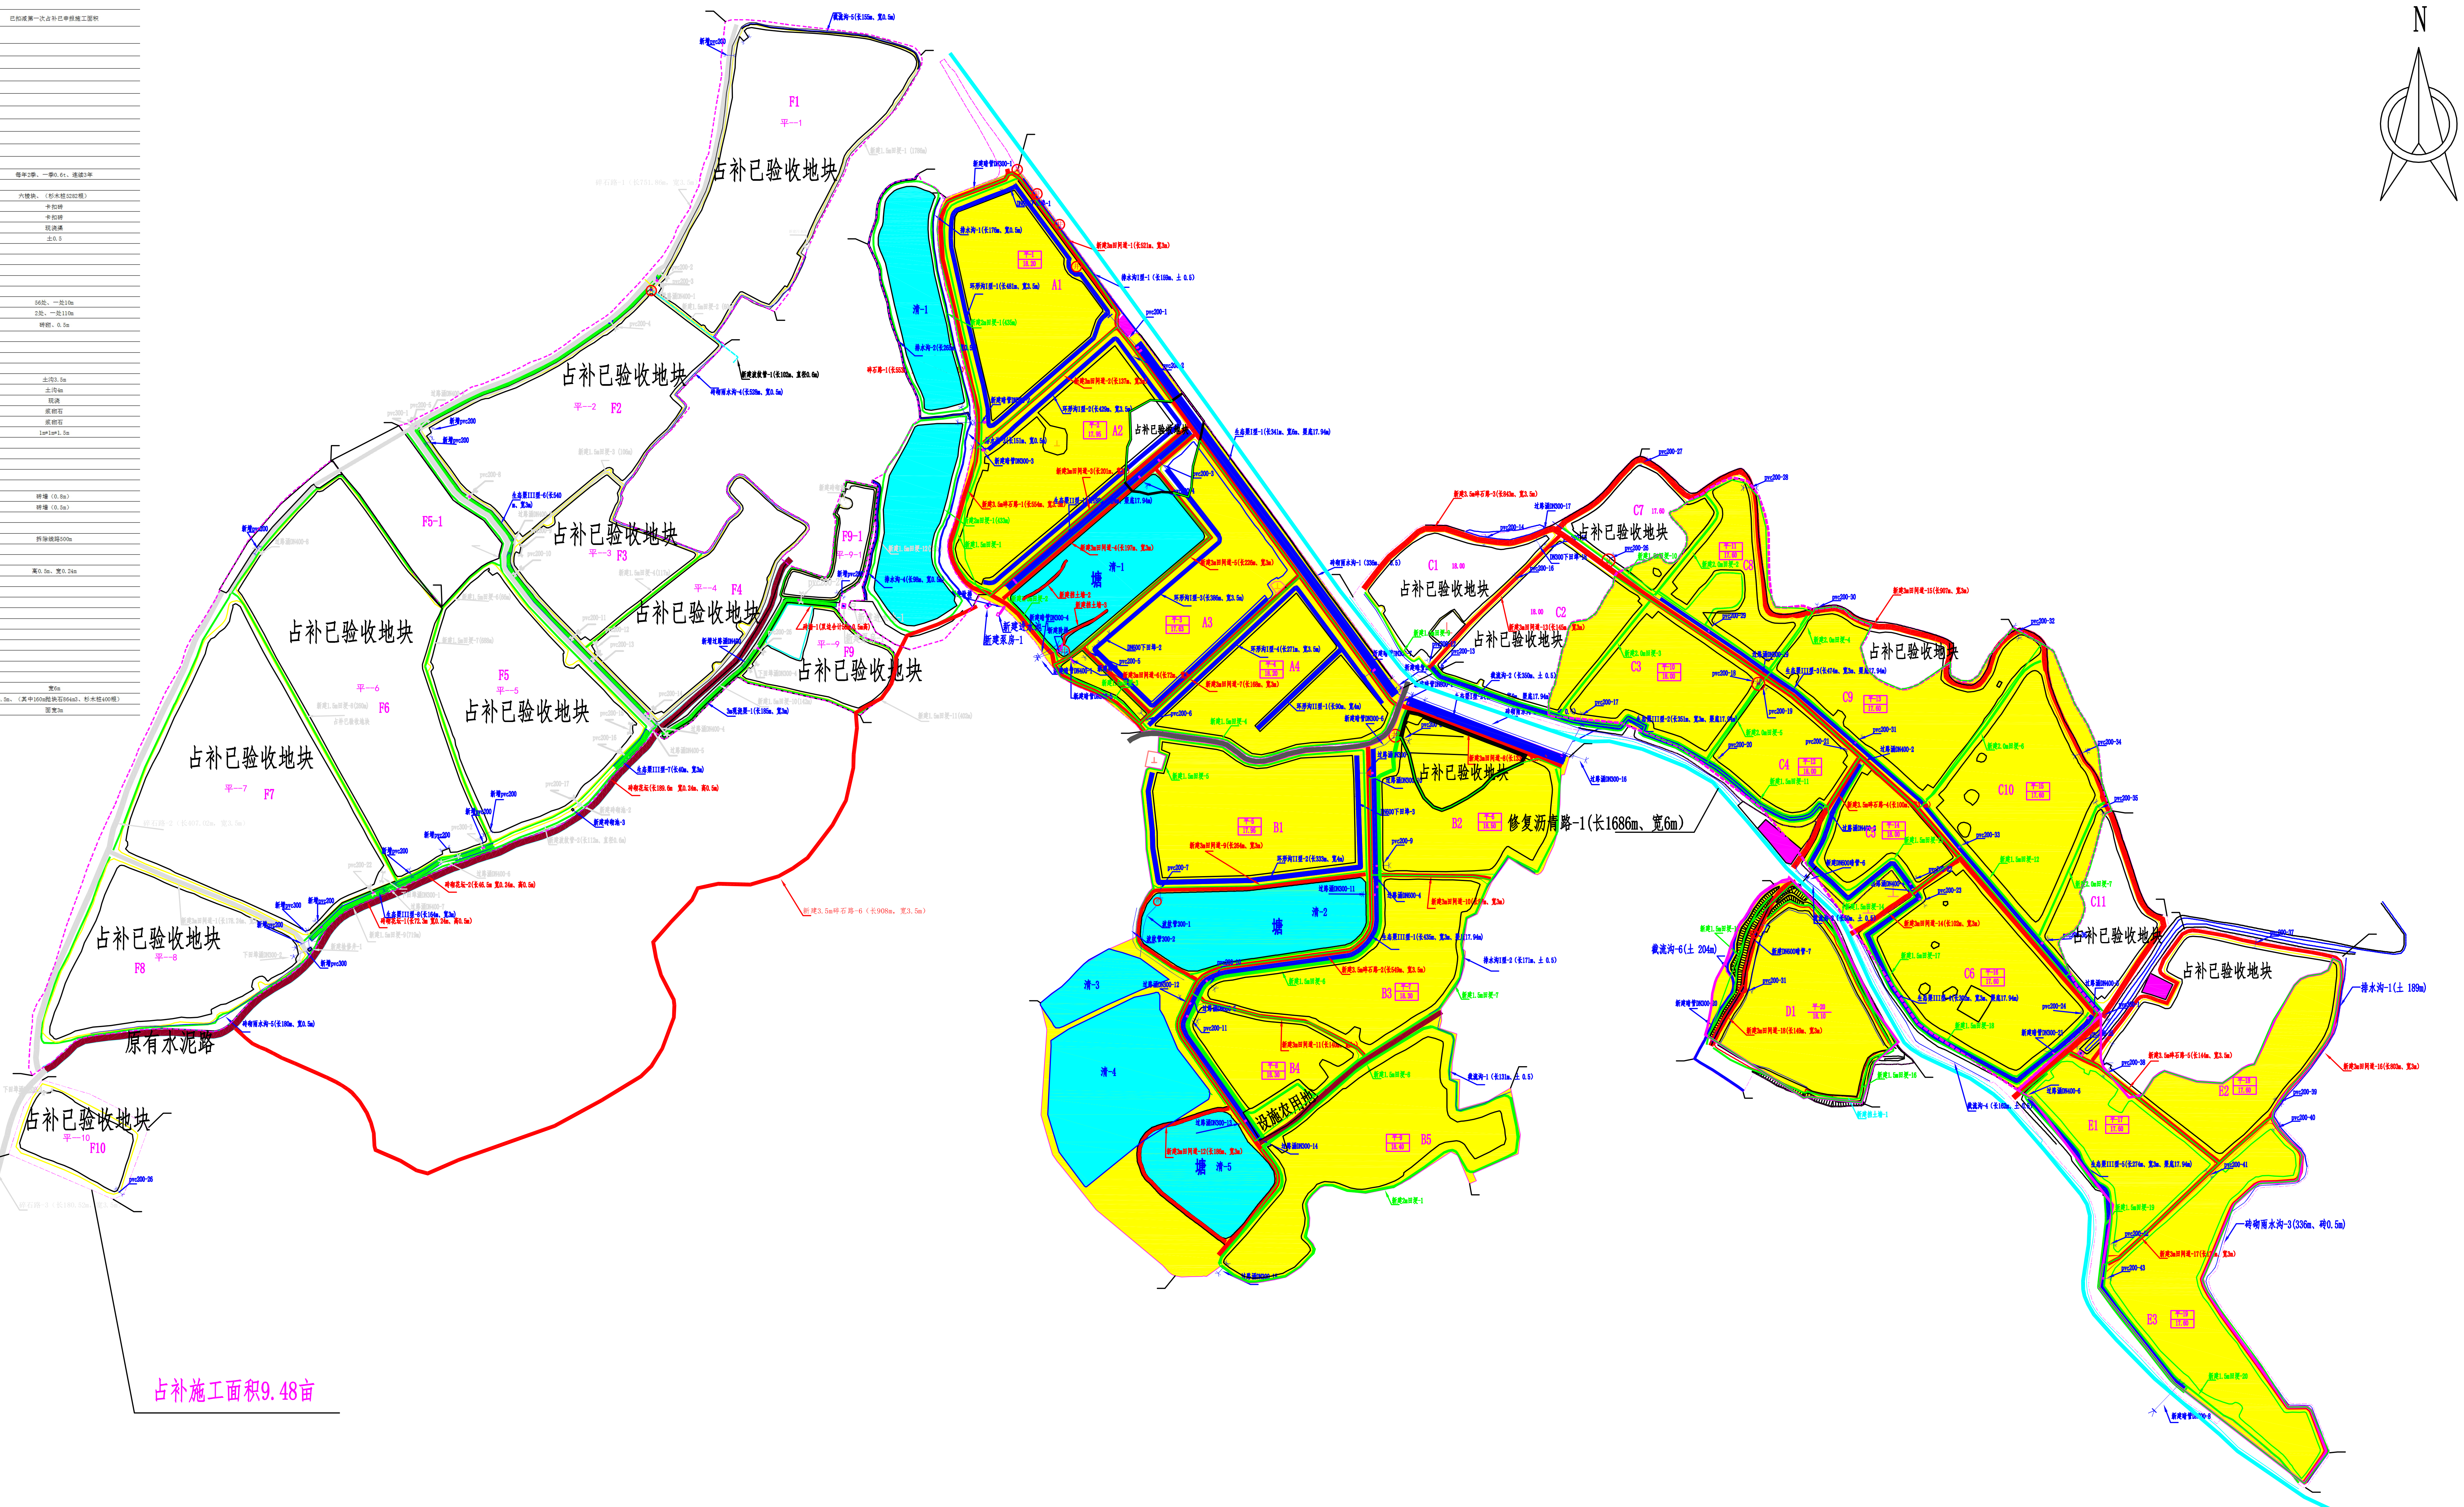

图　例					
项目区界	果　园	水库水面	电 力 线	生态渠I型	新建2m田埂
村　界	乡 村 路	泵　站	抽水平台	生态渠II型	新建1.5m田埂
镇　界	大 车 路	田　坎	清淤沟渠	生态渠III型	新建检查井
已实施项目范围	机 耕 桥	地 类 界	水流方向	新建暗管	新建砖砌池
水　田	涵　洞	小　路	坑　塘	田块编号	新建挡土墙
旱　地	河流水面	通 信 线	双线沟渠	碎石路	修复沥青路
林　地	灌木林地	坟　地	等高线. 高程点	新建3m田间道	
荒 草 地	居 民 点	单线沟渠	注记坐标	新建2.5m田埂	

1:2000

2022年度梁子湖区梁子镇沙湾村提质改造旱改水项目 （2022年度梁子湖区梁子镇全域国土综合整治项目子项目）竣工图-1			
竣工测量单位	**北京跨时空国土规划设计院有限公司**		
审　定	**黄超一**	**测图比例尺**	**1:1000**
校　核	**黄超一**	**打印比例尺**	**1:4000**
测　量	**范　健**	**制图日期**	**2024.12**
制　图	**黄超一**	**图　号**	